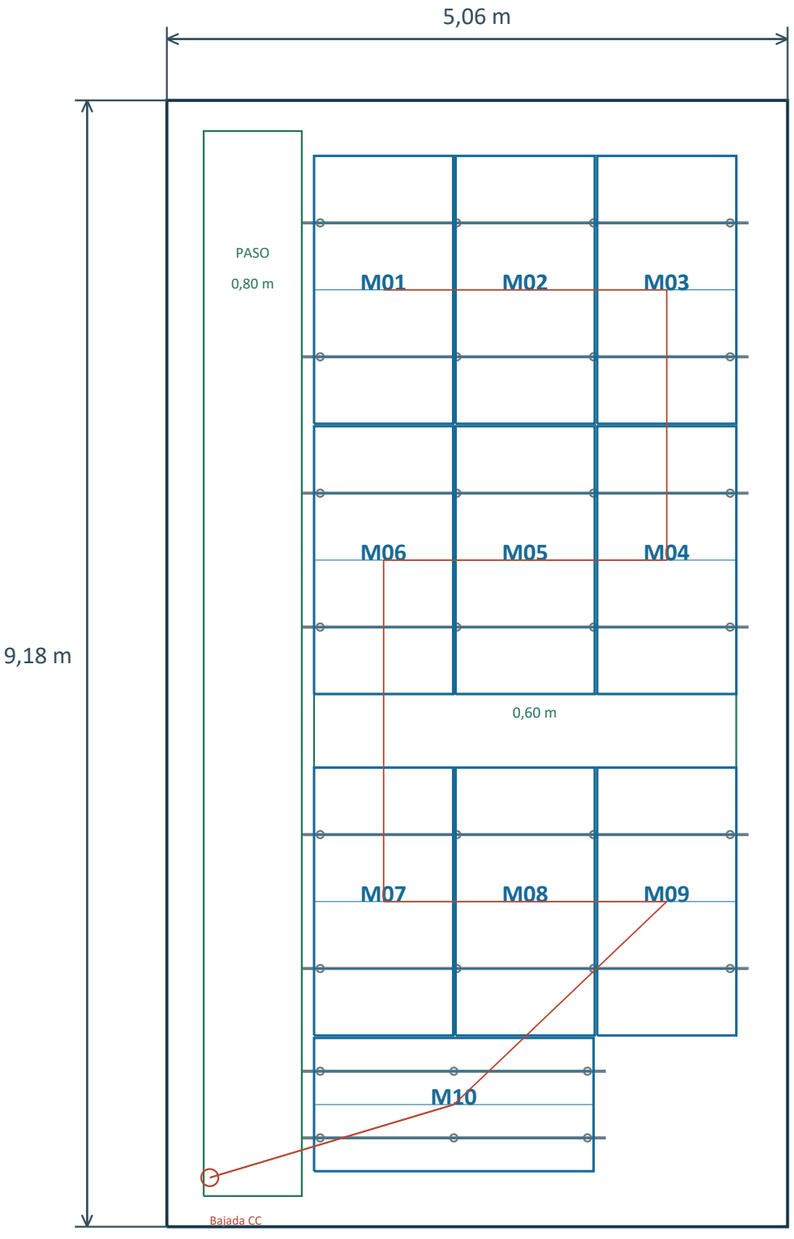


N

10 × 550 Wp = 5,50 kWp · 1 cadena en PV1

Módulo de proyecto 2.279 × 1.134 mm

Pendiente 30 % · β = 16,70° · rumbo alero 91,66°

Franja disponible 5,06 × 9,18 m en planta

Superficie de módulos 25,84 m² · proyección 24,75 m²


LEYENDA DE IMPLANTACIÓN

- M01–M10 módulos y conexión de cadena
- Rieles y puntos de anclaje de diseño
- Bandas reservadas para servicio
- Recorrido de CC y punto de bajada

Sección A–A en el sentido de la pendiente

La sección muestra la pendiente y el montaje coplanar.

Anclajes a estructura resistente y remates según replanteo.

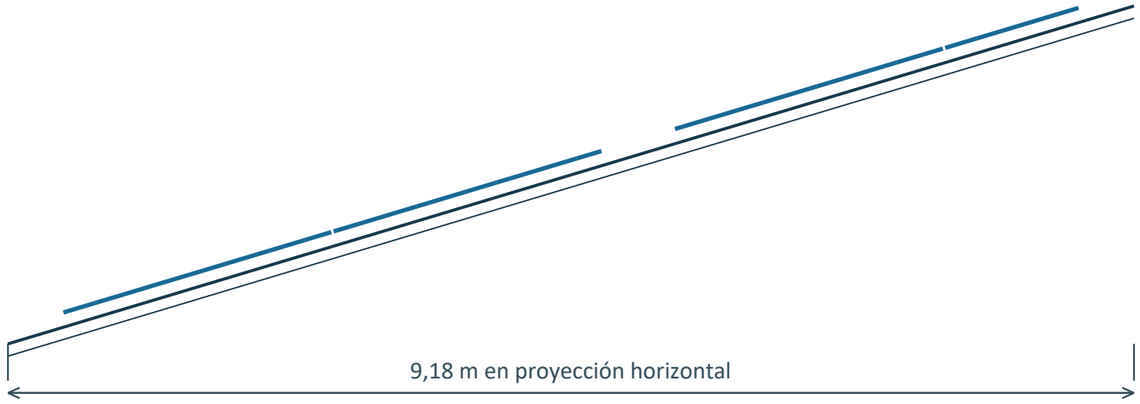

Ocho tramos de riel. Compra de referencia 8 perfiles RS-327 de 4,80 m.

Cantidad de diseño 30 anclajes, 16 grapas finales y 12 intermedias.

Aplicar la ficha Romagnole y verificar el soporte real y el viento NP 196.

Ruta CC de cálculo 25 m de ida. Cable solar Cu 6 mm² por polo.

La localización de la bajada se ajusta en el replanteo de obra.

UNIR · Máster Universitario en Energías Renovables

Autoconsumo fotovoltaico de vivienda en Ciudad del Este

Implantación, anclajes y sección de cubierta

Clara María De Los Ángeles Rolón Duré · Entrega v0.3

INGENIERÍA DE DISEÑO

Unidad del modelo mm

Cotas expresadas en metros

Ubicación exacta reservada

FV-01

Escala 1:50 en A3

RED ANDE

380/220 V · 50 Hz

3F + N

MEDIDA Y PCC

Contador de facturación

Sensor DTSU666-H

TC de cada fase

TABLERO PRINCIPAL

Punto de conexión FV

Protección general existente

a verificar en tablero

Suministro a cargas

CARGAS DE VIVIENDA

3F + N + PE

Reparto de diseño 38/33/29 %

CA 20 m · 5G4 mm² Cu · 8,5 A de cálculo

RS-485 + SDongleA-05 · límite por fase

CC 25 m de ida

GENERADOR FV

10 × YHP550W

Una cadena en serie

501 V Voc STC

SECCIONAMIENTO CC

QCC ≥ 600 V CC / 25 A

DPS FV tipo 2

Ucpv ≥ 600 V

2 × 6 mm² Cu · H1Z2Z2-K

INV1 · HUAWEI M1

SUN2000-5KTL-M1

Corriente alta 13,5/19,5 A

5 kW · 380/220 V

RAMA CA FV

QAC 16 A · 3F + corte N

ID tipo A · 100 mA · 4P

DPS tipo 2 para TT

BARRA PE · equipotencialidad de marcos, rieles, inversor y tableros

Electrodo TT · objetivo RA ≤ 10 Ω

Ajustes de red, poder de corte y tierra según ANDE y ensayo.

Habilitar estado seguro a 0 % ante pérdida de medida.

Conservar la separación N–PE en el esquema TT del usuario.

Esquema de diseño. Los equipos CC permanecen energizados bajo irradiación.

UNIR · Máster Universitario en Energías Renovables

Autoconsumo fotovoltaico de vivienda en Ciudad del Este

Esquema unifilar, conductores, protecciones y control

Clara María De Los Ángeles Rolón Duré · Entrega v0.3

INGENIERÍA DE DISEÑO

Unidad del modelo mm

Cotas expresadas en metros

Ubicación exacta reservada

FV-02

Escala S/E